
蓝莓加工厂 / 自主布局 V1.2 · 工艺物流贯通

20t/天设计条件 · 非Native确定性生成 · 条件性概念设计，非施工图

A1横版 / 1:200 / mm

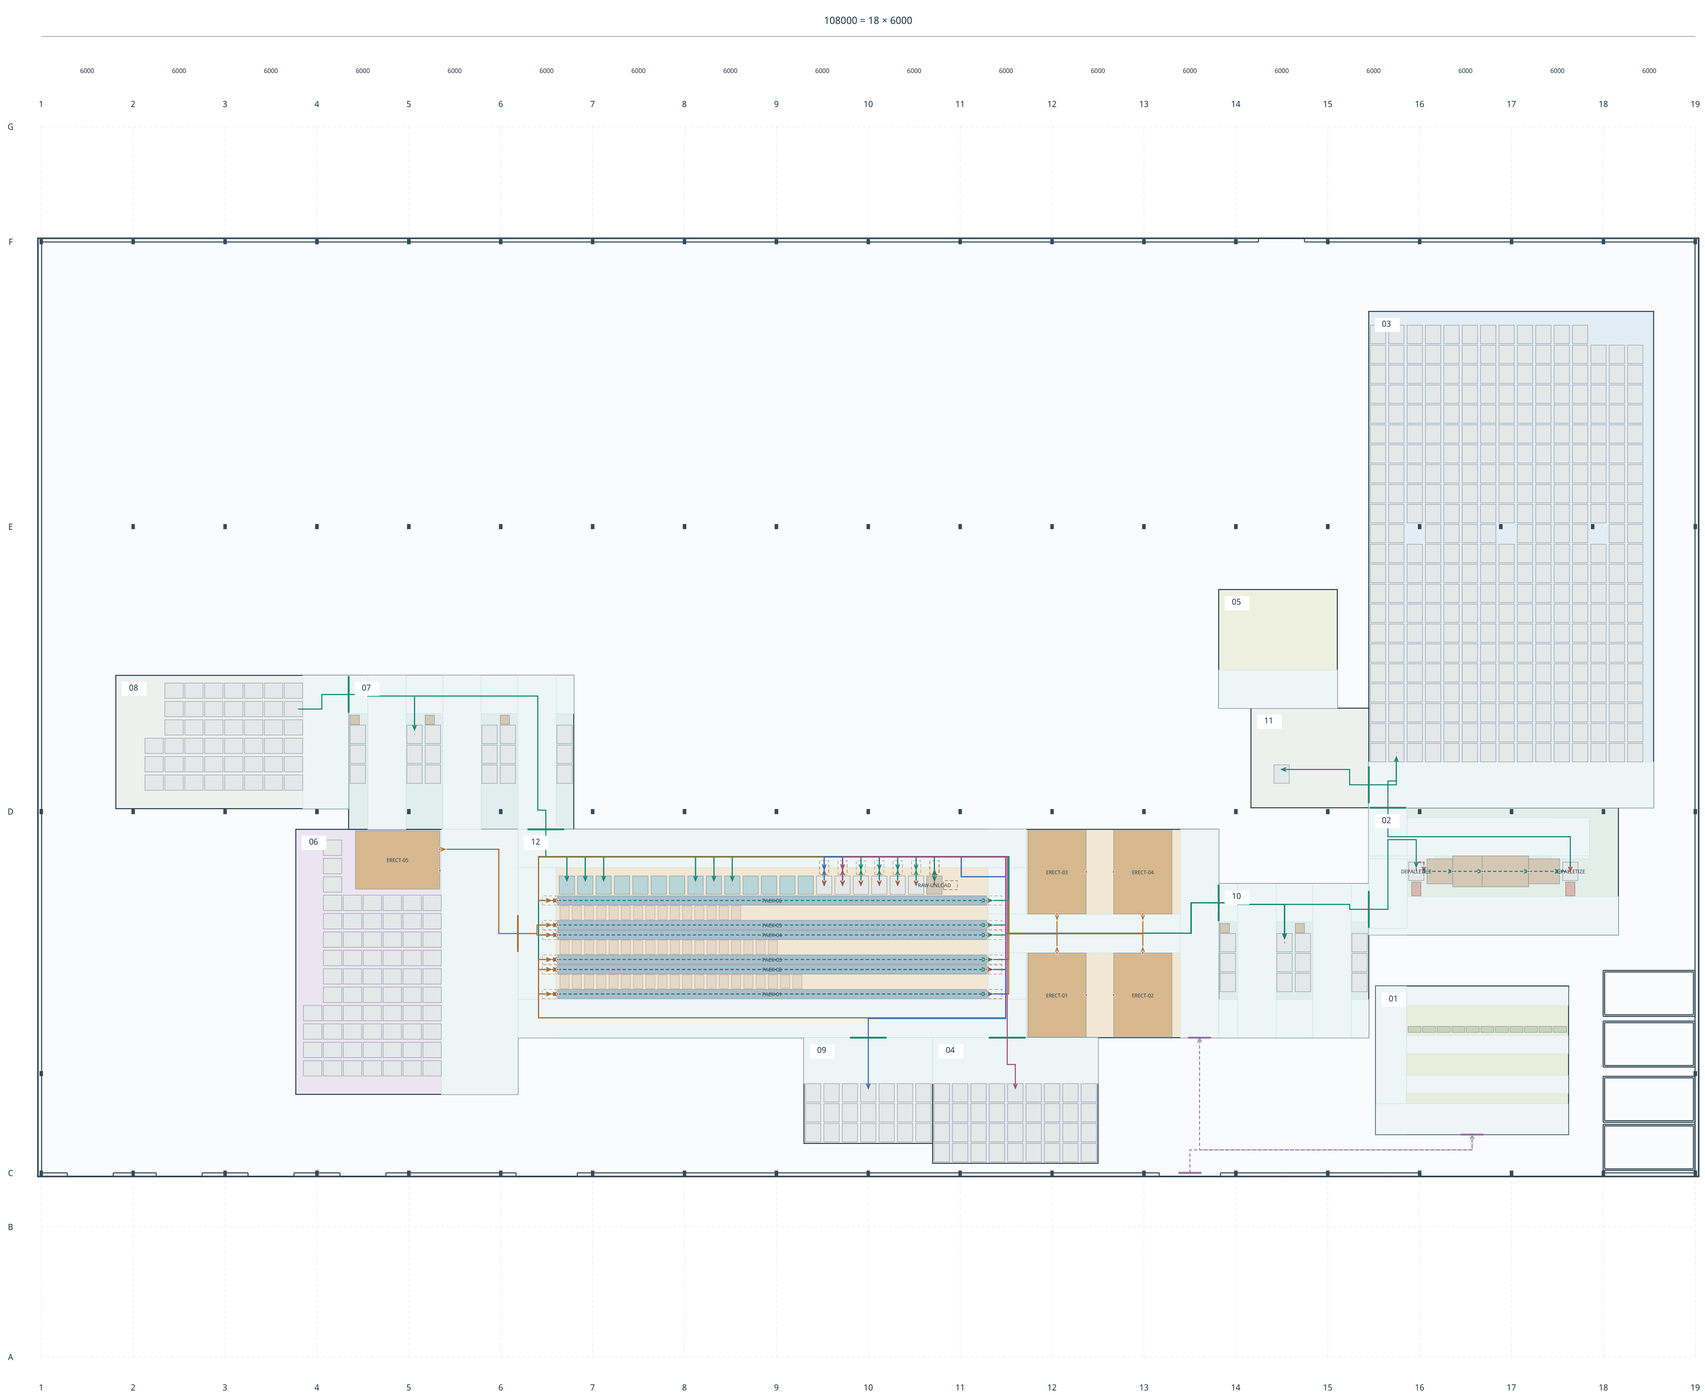

20m校尺段 = 100mm纸面长度 / 按100%打印

数据源为同次计算坐标；未贯通路线不绘制完整箭头。所有结构柱保留。

候选Hash：sha256:188083411deb269eeebf3545862313480 5acd37acbdae5fd67be543ad194eff0

12区 · 真实计算尺寸

01 更衣室
12600 × 9700 / 122.220㎡

02 覆膜间
16300 × 8300 / 135.290㎡

03 成品间
18600 × 32400 / 602.640㎡

04 冻果间
10800 × 8200 / 88.560㎡

05 办公室
7746 × 7746 / 60.001㎡

06 包材库
14500 × 17300 / 250.850㎡

07 一级预冷间
14700 × 10050 / 147.735㎡

08 原果暂存间
15200 × 8700 / 132.240㎡

09 次果暂存间
8400 × 6900 / 57.960㎡

10 二级预冷间
9800 × 10050 / 98.490㎡

11 出货通道
7693 × 6500 / 50.005㎡

12 分选包装间
45760 × 13600 / 622.336㎡

候选状态：CONDITIONAL_PROCESS_CANDIDATE

主产品完整条件链 6/6

设备路线 91通过 / 0未贯通

绿色：六线产品；蓝色：次果；玫色：冻果

虚线机内/人工交接：条件操作，非厂家通过

褐色：成箱配送 / 紫虚线：纸板补给

紫色：人员路径 / 红点：待审设备接口

14待冷缓冲位与6包装工作位分别计数

N/S为两服务组，重排于本方案北侧工作带

主通道2500；包材主通道5000（mm）

托盘车及载荷1300×1800为待审假设

转向2222方包络 ≠ 真实车辆运动学

操作点600×900为未批准几何假设

共用通道需调度；未证明同时交通/20t吞吐

储存：保留原有序取放，非任意直接存取

Truck、完整P2D及工程批准未成立

六线完整链的几何中心线长度

PACK-01 279.852m / CONTINUOUS

PACK-02 274.250m / CONTINUOUS

PACK-03 270.548m / CONTINUOUS

PACK-04 255.346m / CONTINUOUS

PACK-05 251.644m / CONTINUOUS

PACK-06 246.042m / CONTINUOUS

长度含一次代表性缓冲与处理段；非吞吐指标

封膜机内部输送由声明接口连接，厂家能力待确认