
蓝莓加工厂 · 程序自主整厂布局 A

20t/天 · 原建筑结构约束 + 原P1尺寸规则 · 独立生成坐标 / 条件性概念设计，非施工图

A1 横版 1:200

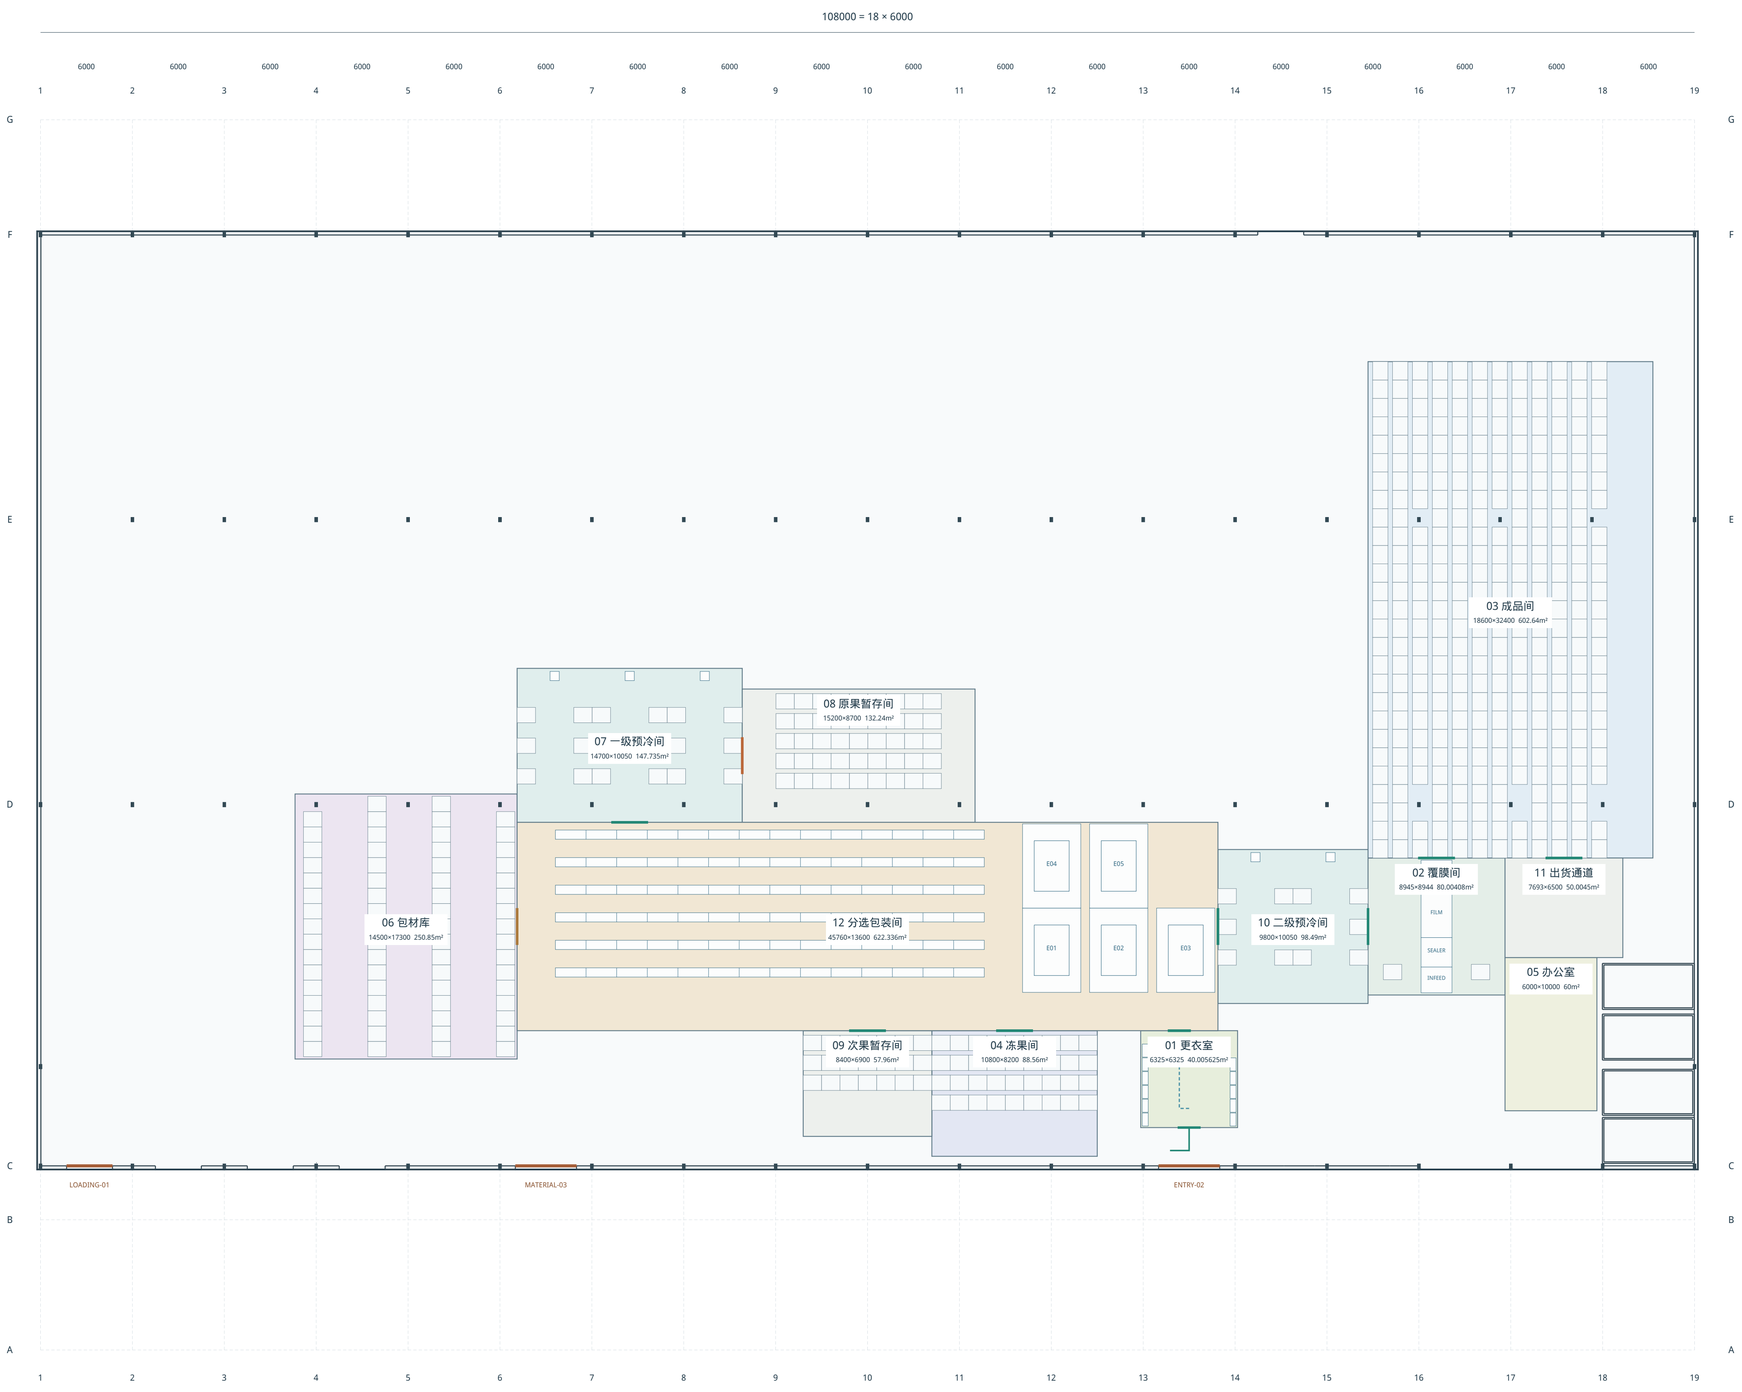

20m校尺段 = 100mm纸面长度；按100%打印，勿适合页面。

结果 sha256:077a07f8ecdde8c93a7567db112fd34f7595668d68dcb1394012769 9dd50f977

独立计算结果

01 更衣室
6325 × 6325 mm / 40.005625m²

02 覆膜间
8945 × 8944 mm / 80.00408m²

03 成品间
18600 × 32400 mm / 602.64m²

04 冻果间
10800 × 8200 mm / 88.56m²

05 办公室
6000 × 10000 mm / 60m²

06 包材库
14500 × 17300 mm / 250.85m²

07 一级预冷间
14700 × 10050 mm / 147.735m²

08 原果暂存间
15200 × 8700 mm / 132.24m²

09 次果暂存间
8400 × 6900 mm / 57.96m²

10 二级预冷间
9800 × 10050 mm / 98.49m²

11 出货通道
7693 × 6500 mm / 50.0045m²

12 分选包装间
45760 × 13600 mm / 622.336m²

验证范围

12区 / 原7条MUST / 房间互不重叠

原P1尺寸与面积规则保持不变

原非货车Access：11/11

柱体保留；净面积损失见JSON

Truck、完整P2D：未通过 / 未验证

设备主体：包装线6/6

折箱机5/5，整柜11/11

冷却性能、维护、53人流程未验收

绿/橙/褐/紫：产品/原果/包材/人员

蓝虚线：扣除设备后的已查室内段

棕色：原建筑开口，使用分配待审

门喉连接、未画室内段未验证

底图仅含原建筑墙柱及轴网

没有使用Owner功能分区/设备坐标

未分配区域保留，不虚构功能房间

实测尺寸精度受原PDF矢量限制

不是施工图或整厂工程批准