
蓝莓加工厂 · 自主布局 A1

房间—设备—货位—门洞联合迭代 / 20t/天 / 条件性概念方案，非施工图

A1横版 · 1:200 · mm

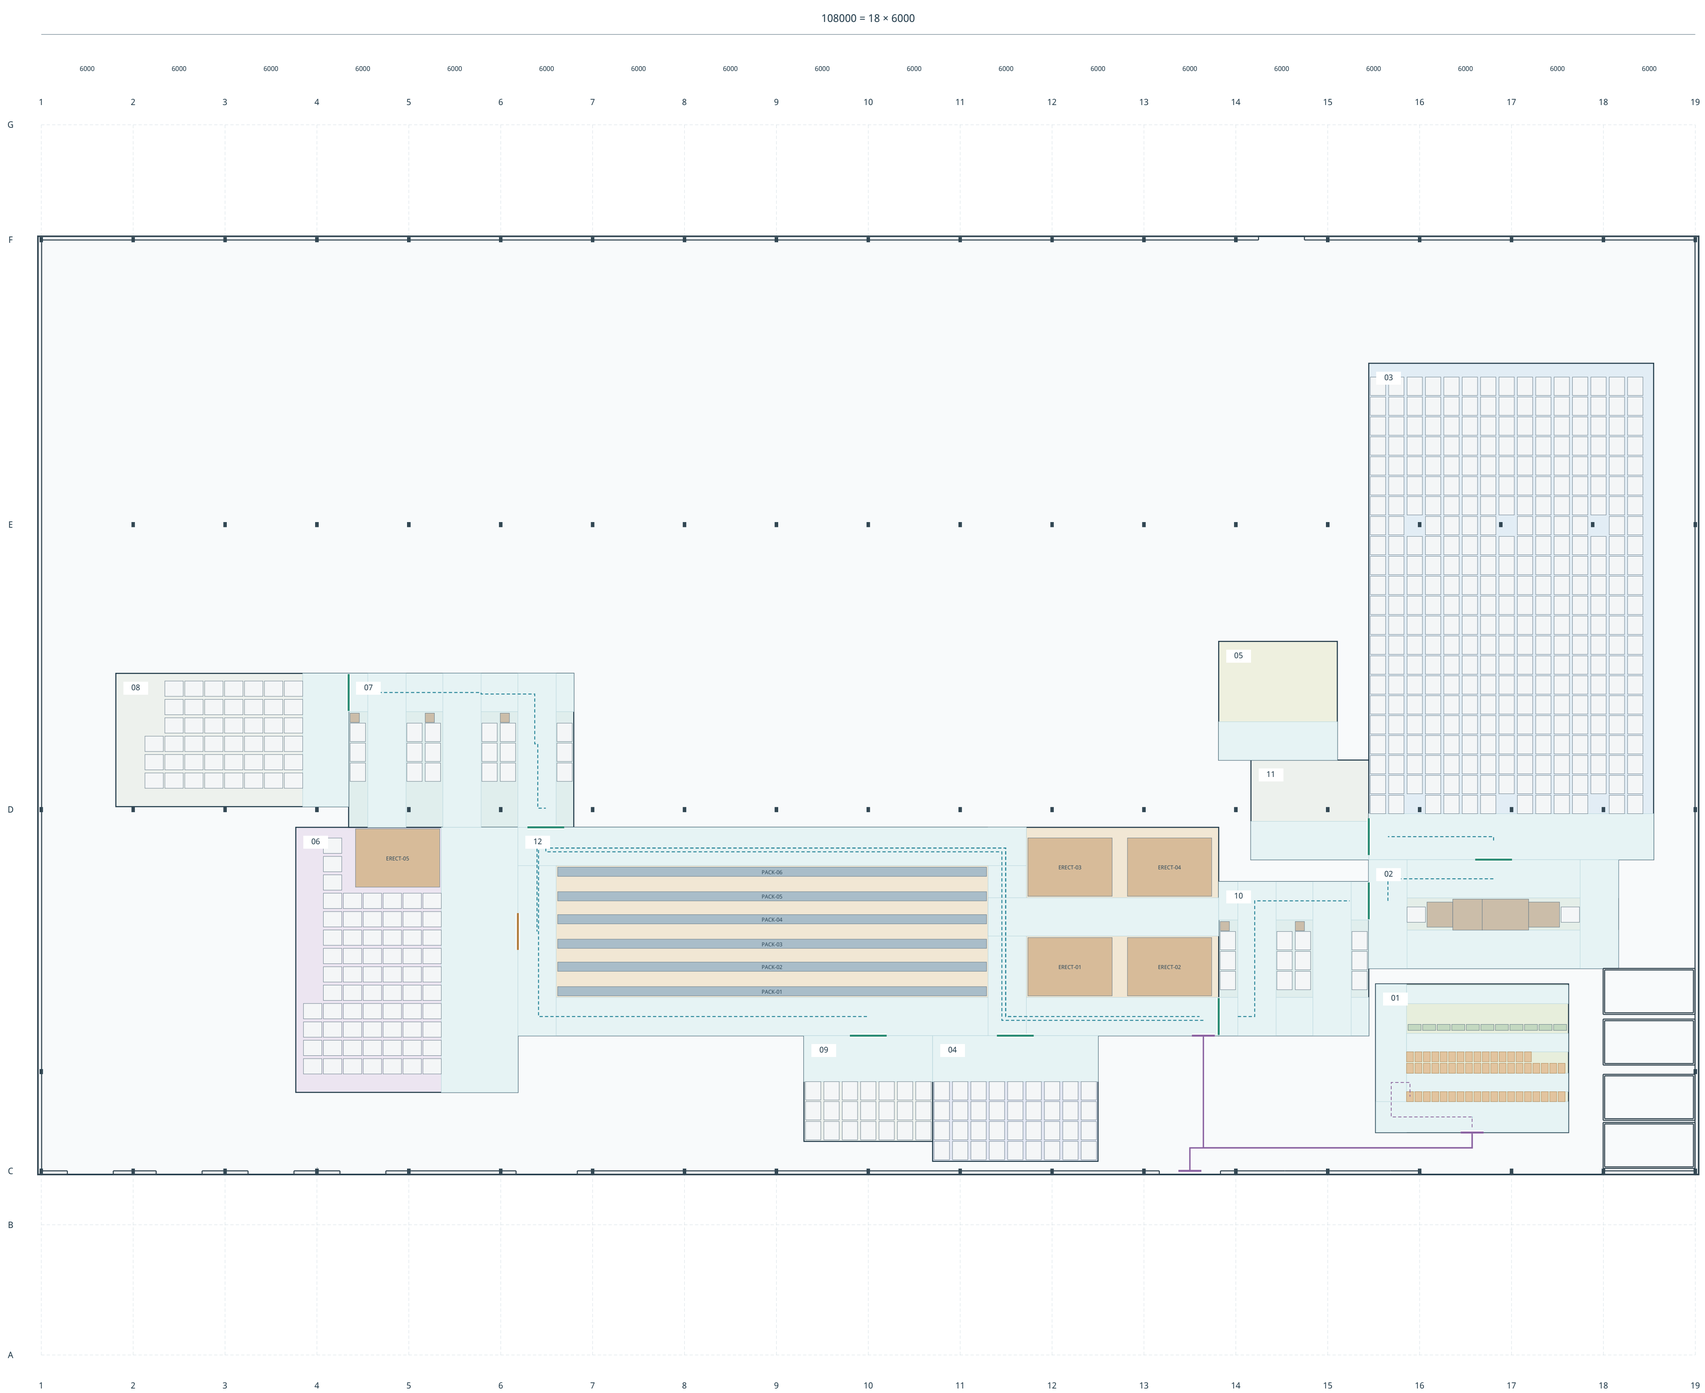

20m校尺段 = 100mm纸面长度 / 按100%打印

同次计算的房间、设备、货位与路线；原建筑未分配部分保留空白。

候选Hash：sha256:f4c3e6903b20261d2695878a7d68964a782e58d00e92dcd9fdaf44f74f002e0d

12区实际计算坐标

01 更衣室
12600 × 9700 / 122.220㎡

02 覆膜间
16300 × 7100 / 115.730㎡

03 成品间
18600 × 32400 / 602.640㎡

04 冻果间
10800 × 8200 / 88.560㎡

05 办公室
7746 × 7746 / 60.001㎡

06 包材库
14500 × 17300 / 250.850㎡

07 一级预冷间
14700 × 10050 / 147.735㎡

08 原果暂存间
15200 × 8700 / 132.240㎡

09 次果暂存间
8400 × 6900 / 57.960㎡

10 二级预冷间
9800 × 10050 / 98.490㎡

11 出货通道
7693 × 6500 / 50.005㎡

12 分选包装间
45760 × 13600 / 622.336㎡

联合计算结果

12区 / MUST 7条 / 原非货车Access 11/11

设备：包装线6/6 · 折箱机5/5 · 整柜11

门前主体冲突：0

已验证室内全宽路线：10

浅蓝：保留通道；蓝虚线：已查室内段

绿：产品；褐：包材；紫：人员

仓储：有顺序的取放几何见证

包材库 67 / 最低67

成品间 324 / 最低315

原果暂存间 45 / 最低37

次果暂存间 21 / 最低19

冻果间 36 / 最低34

非任意直接取放；搬运设备运动学待审

更衣室：53本位 / 两班独立柜位

600×900活动、450×650人体为未批准假设

实际柜门、储物、卫生及维护输入仍缺失

Truck、完整P2D及工程批准未成立